


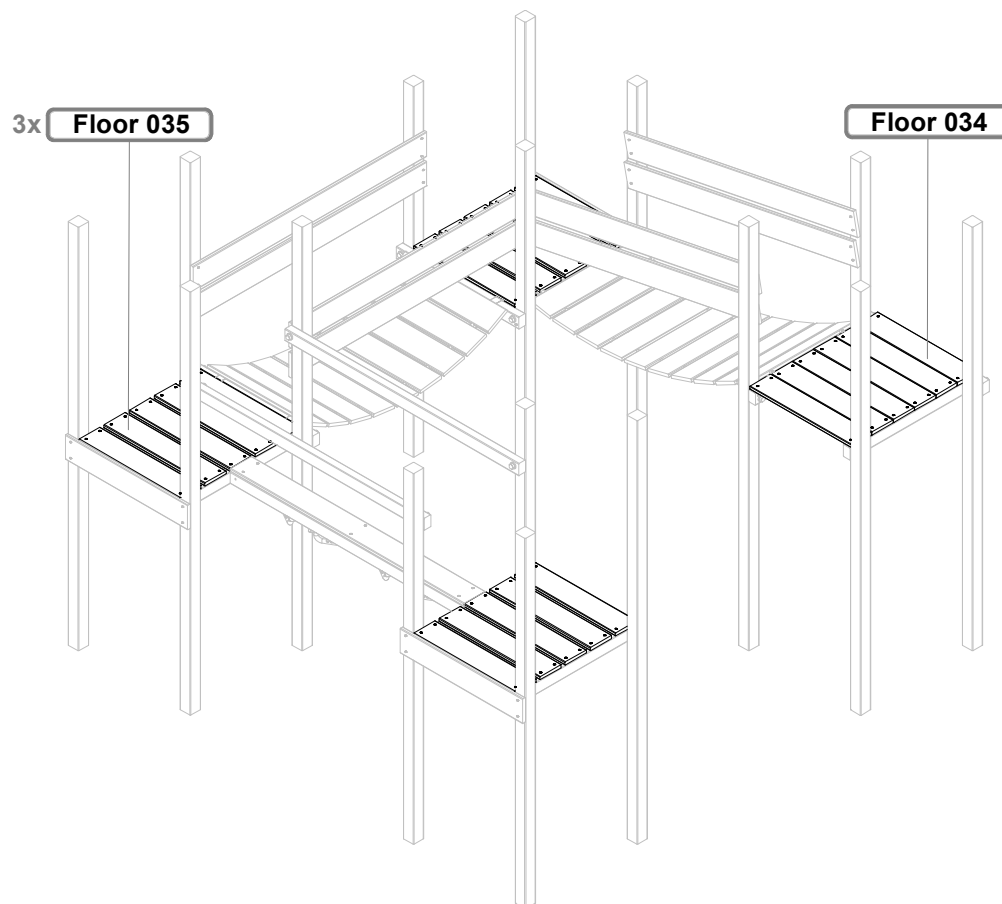
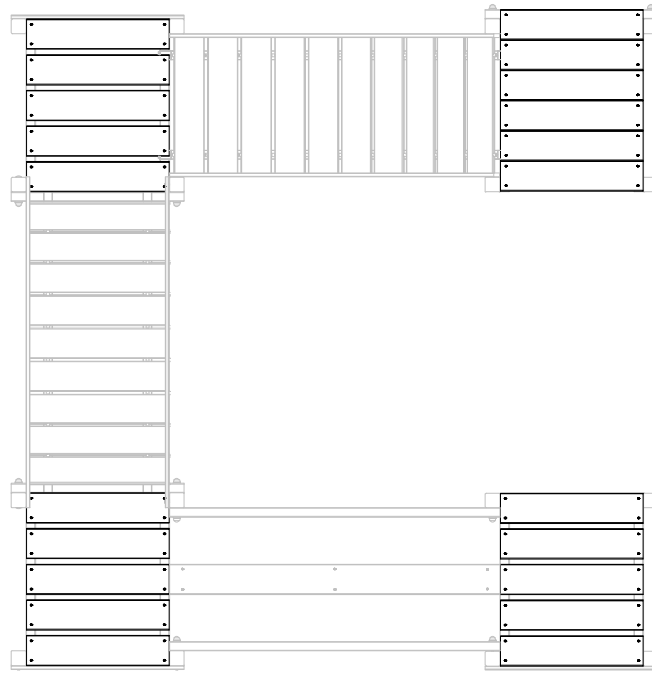
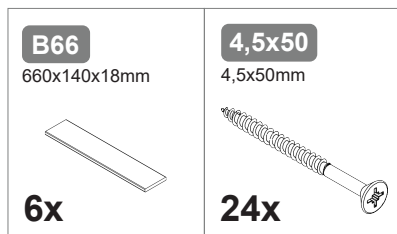
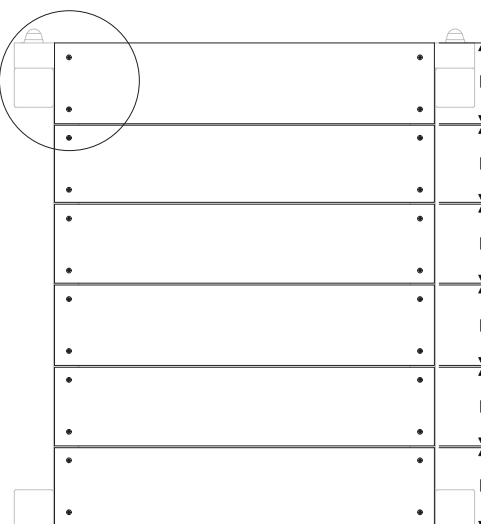
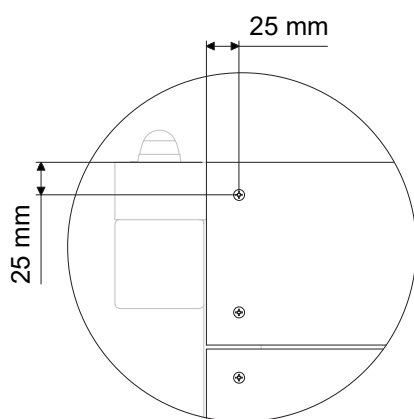


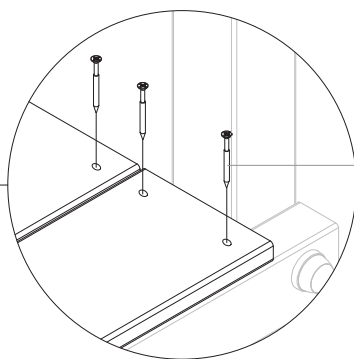


Floor 034 & 035



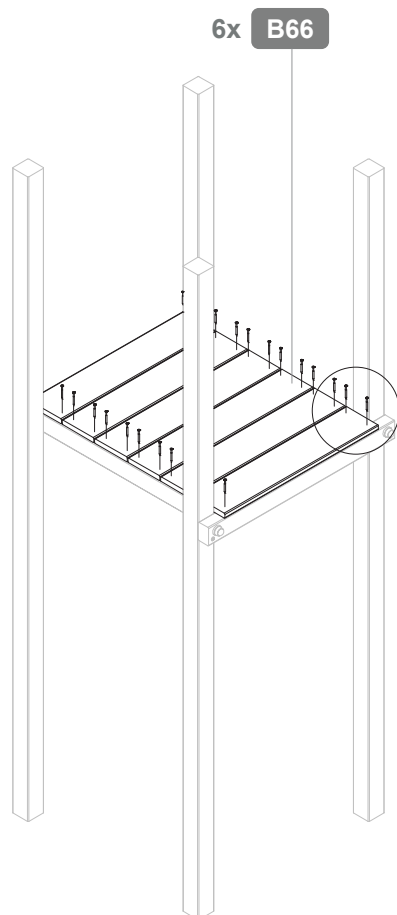


1


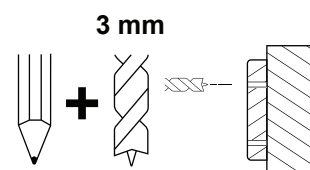


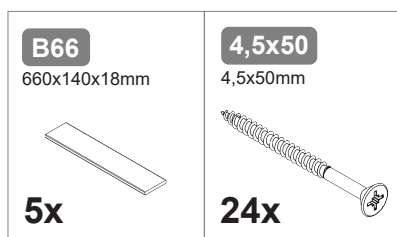


1

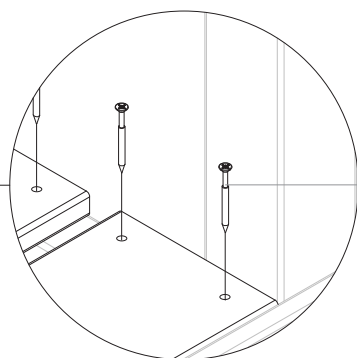
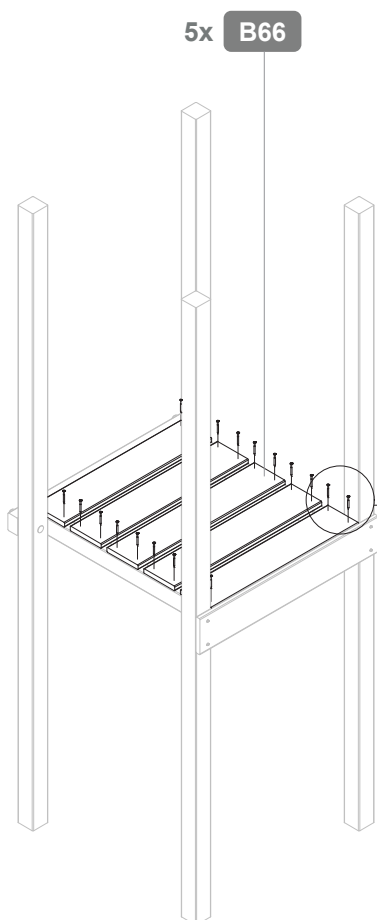
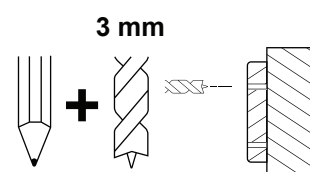




24x
4,5x50


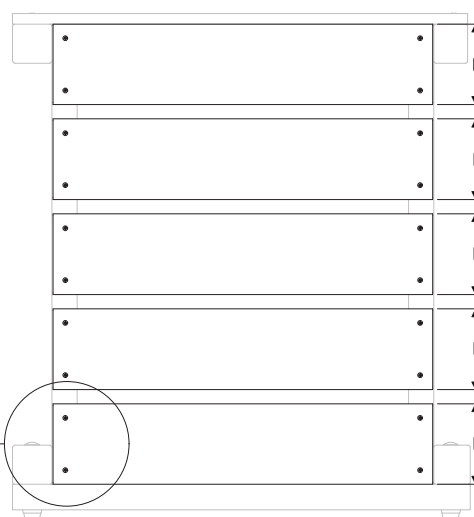
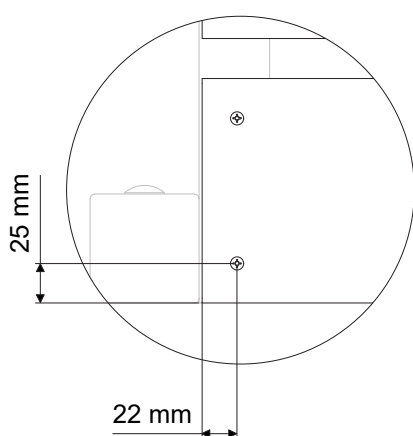



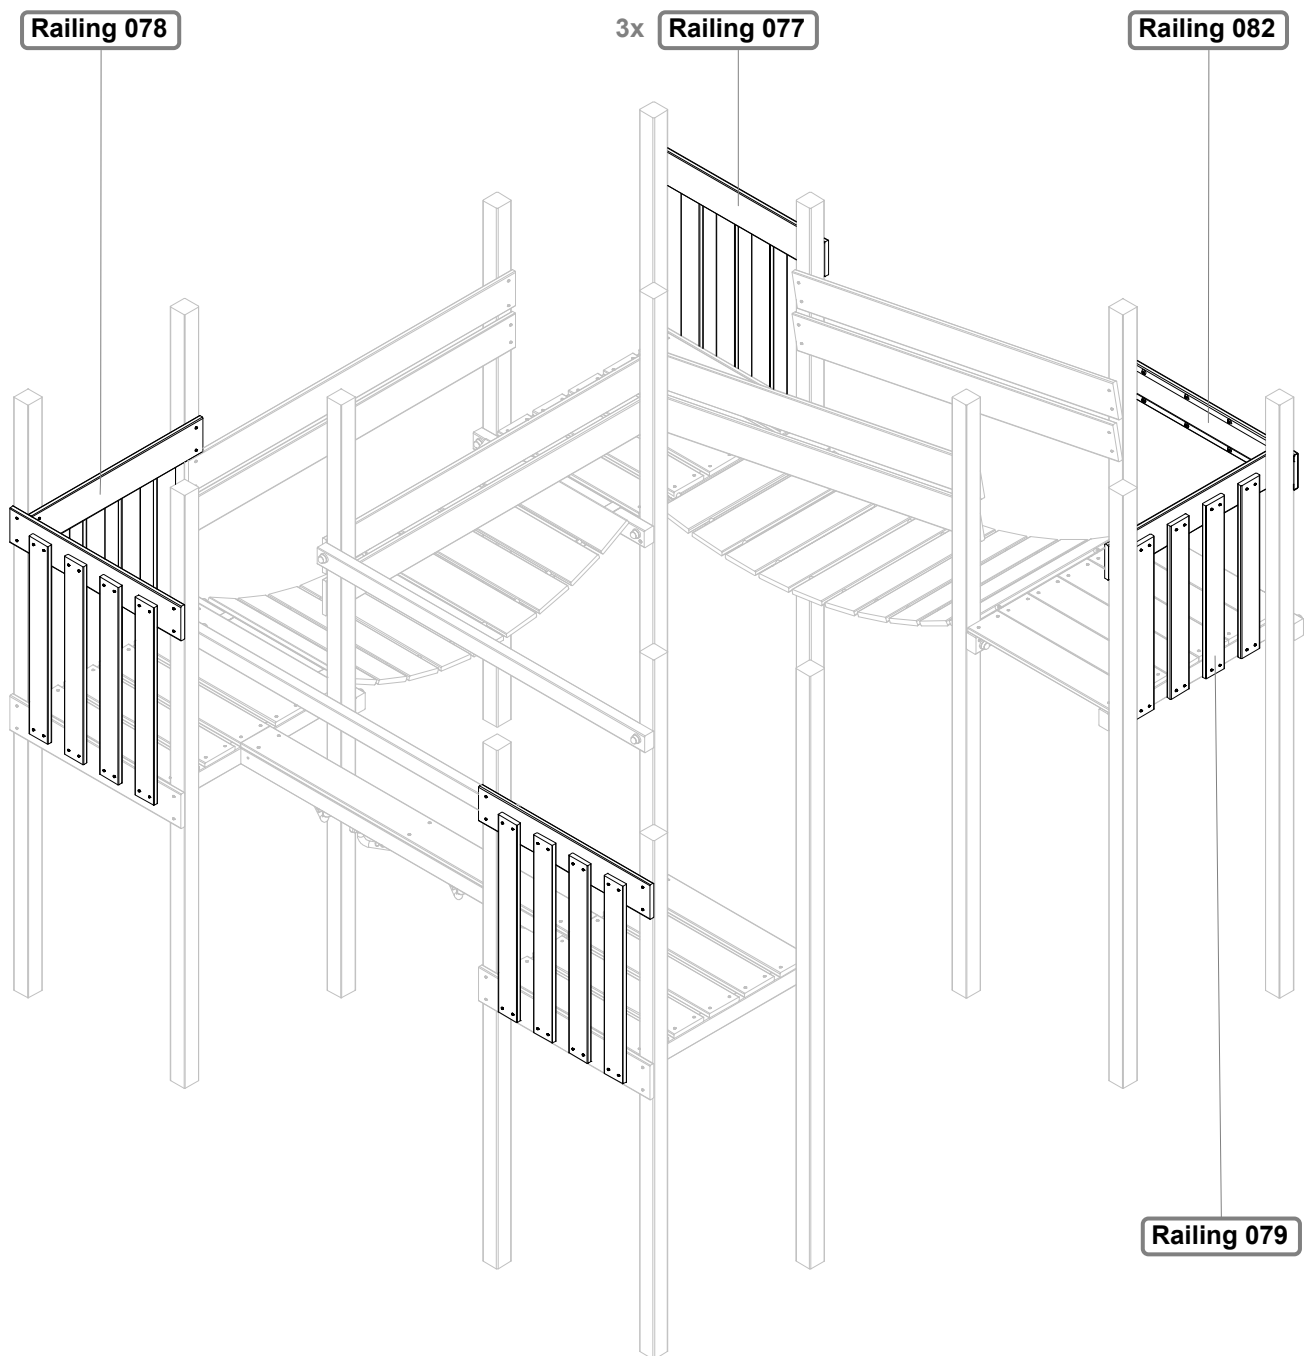




Railing 077,078,079 & 082

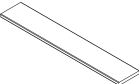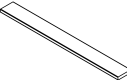
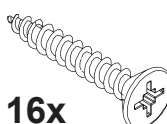
B80 800x140x18mm  1x	L80 800X88X18mm  4x	4,5x50 4,5x50mm  4x	4x30 4x30mm  16x
--	---	---	--

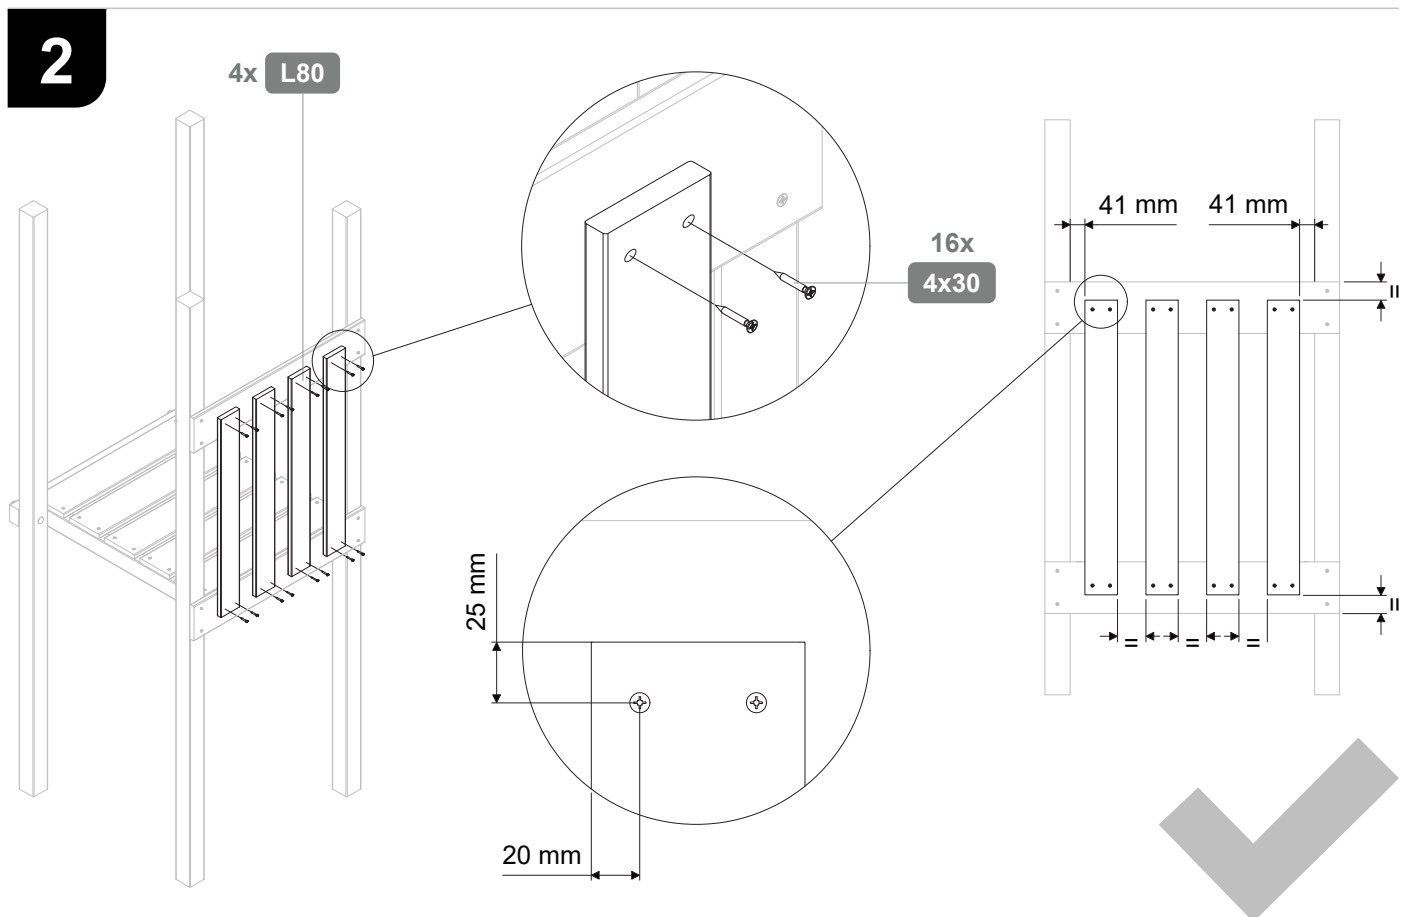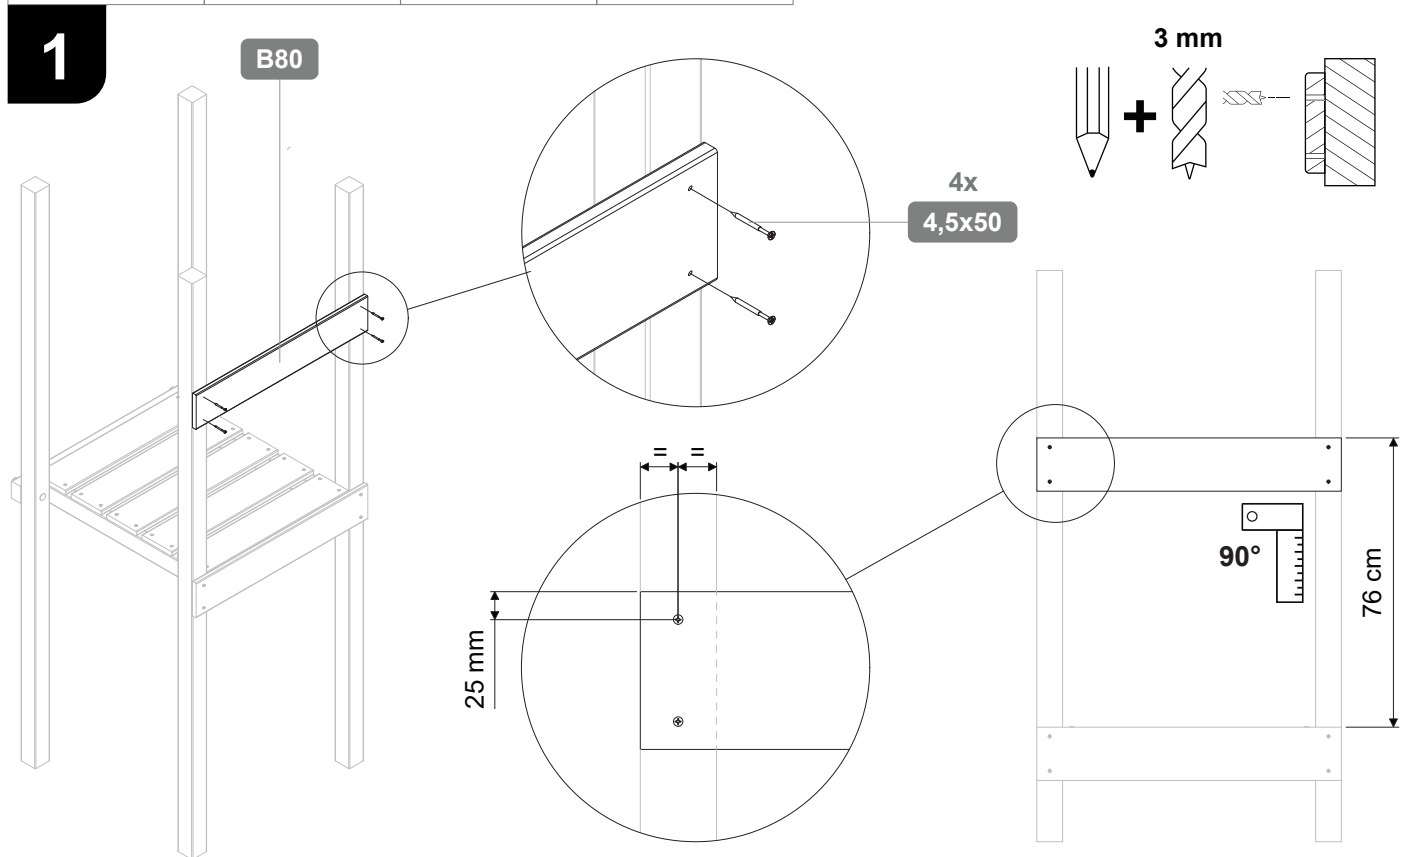

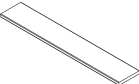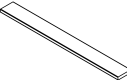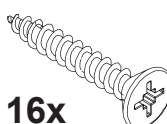B80 800x140x18mm  1x	L80 800X88X18mm  4x	4,5x50 4,5x50mm  12x	4x30 4x30mm  16x
--	---	--	--

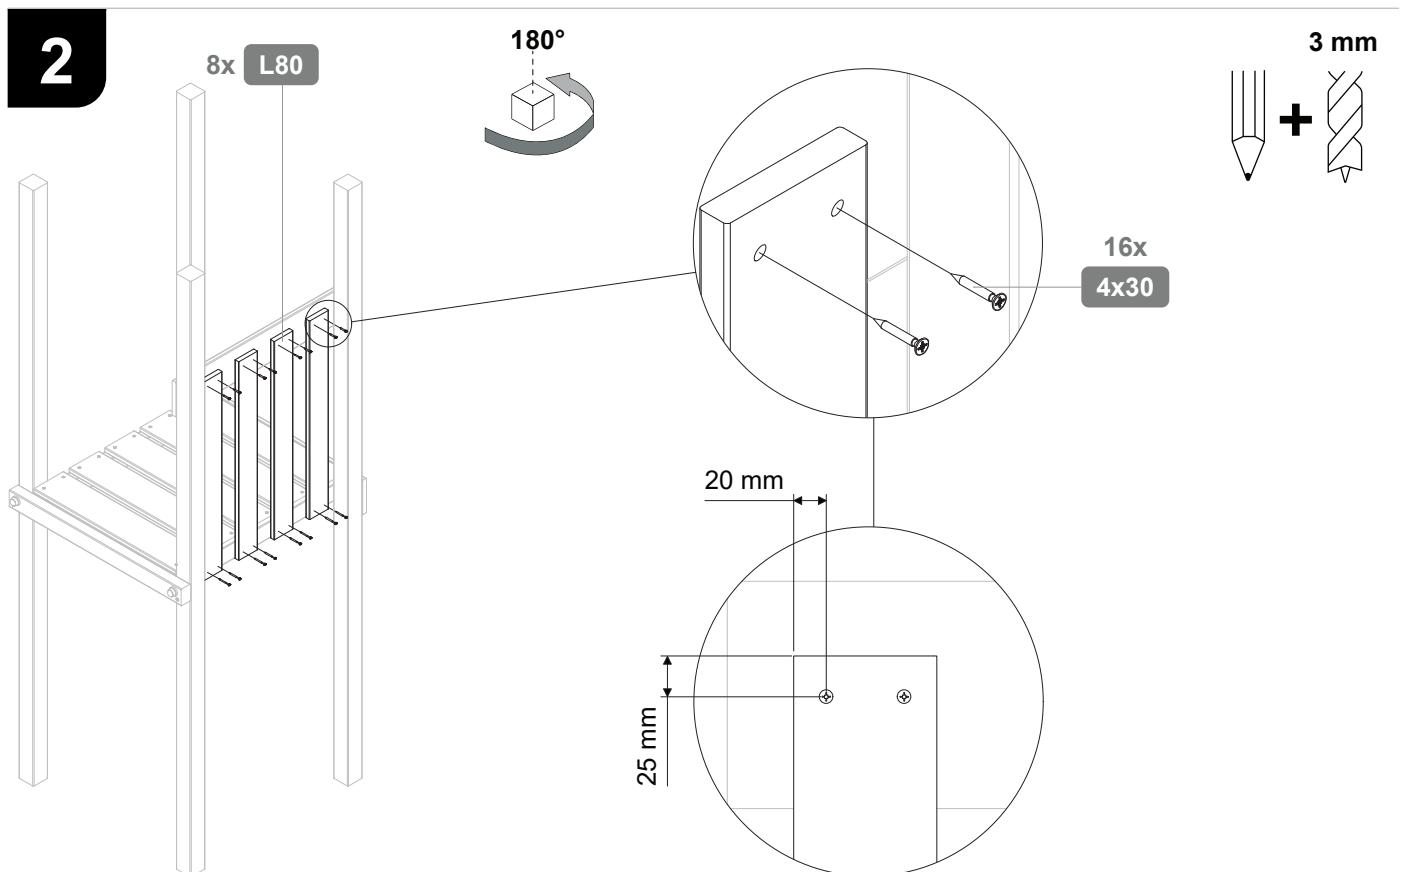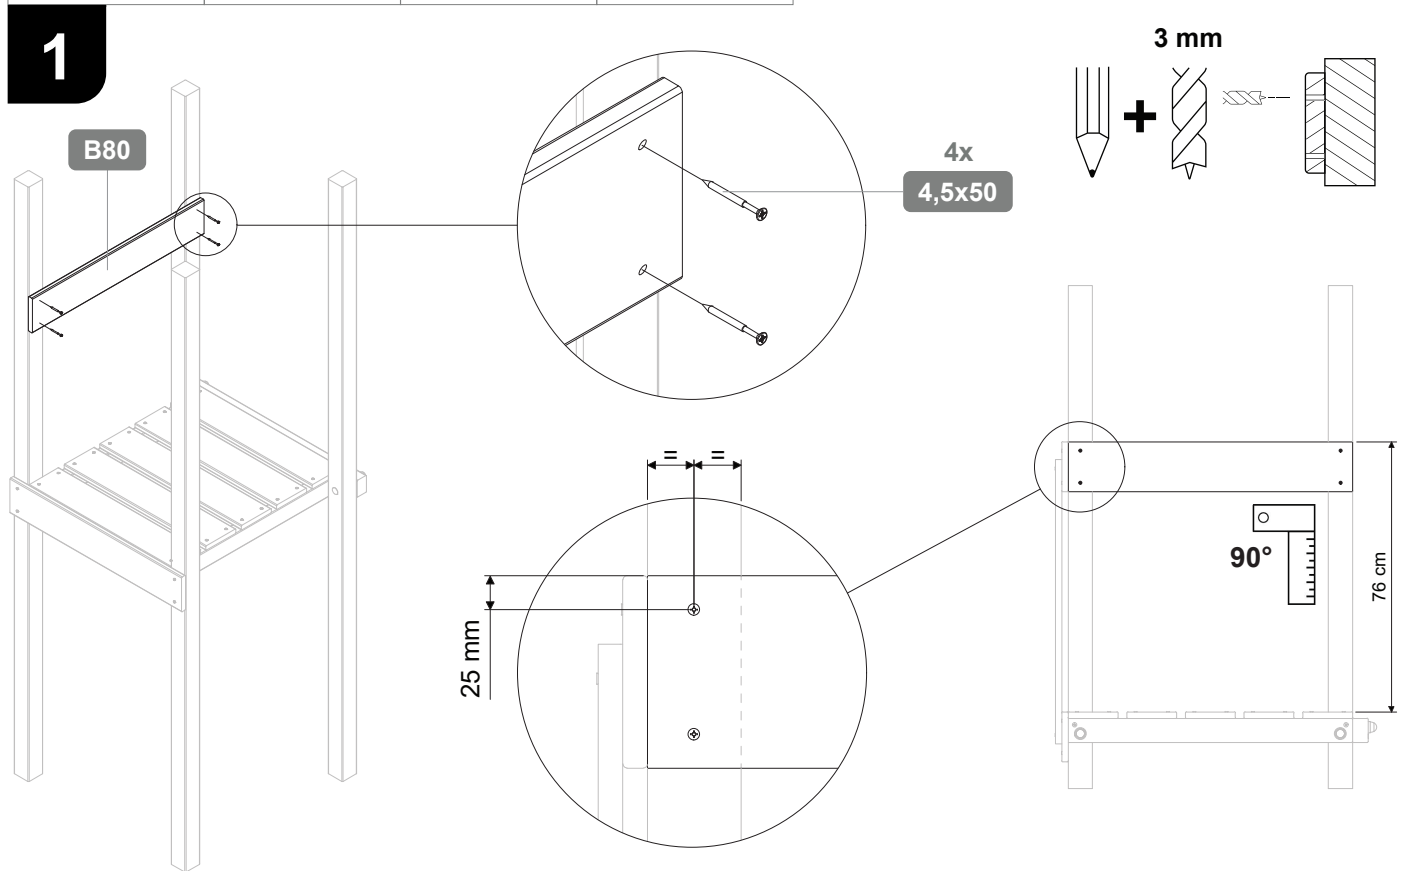

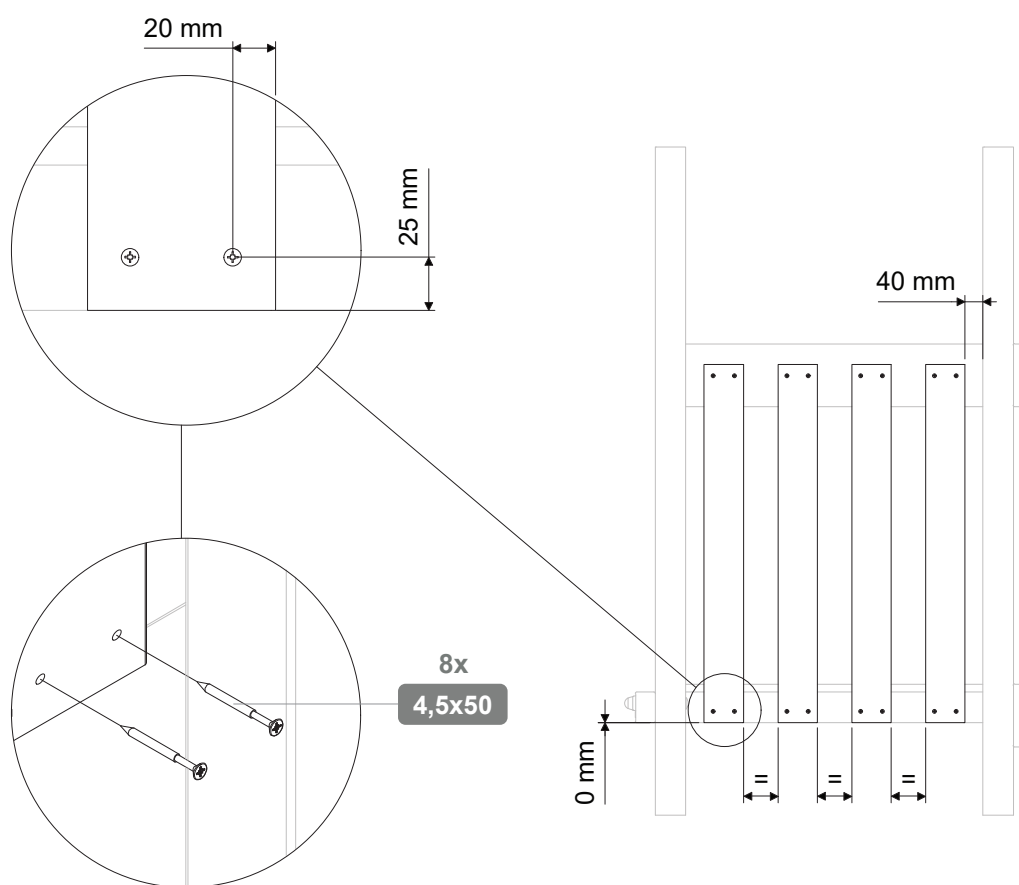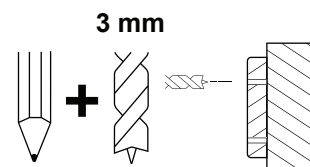

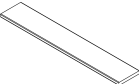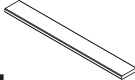B80 800x140x18mm  1x	L70 Insert spec  4x	4,5x50 4,5x50mm  12x	4x30 4x30mm  8x
--	---	--	---

